

PLANCHE 1 / 10 – VUE EN PLAN – IMPLANTATION

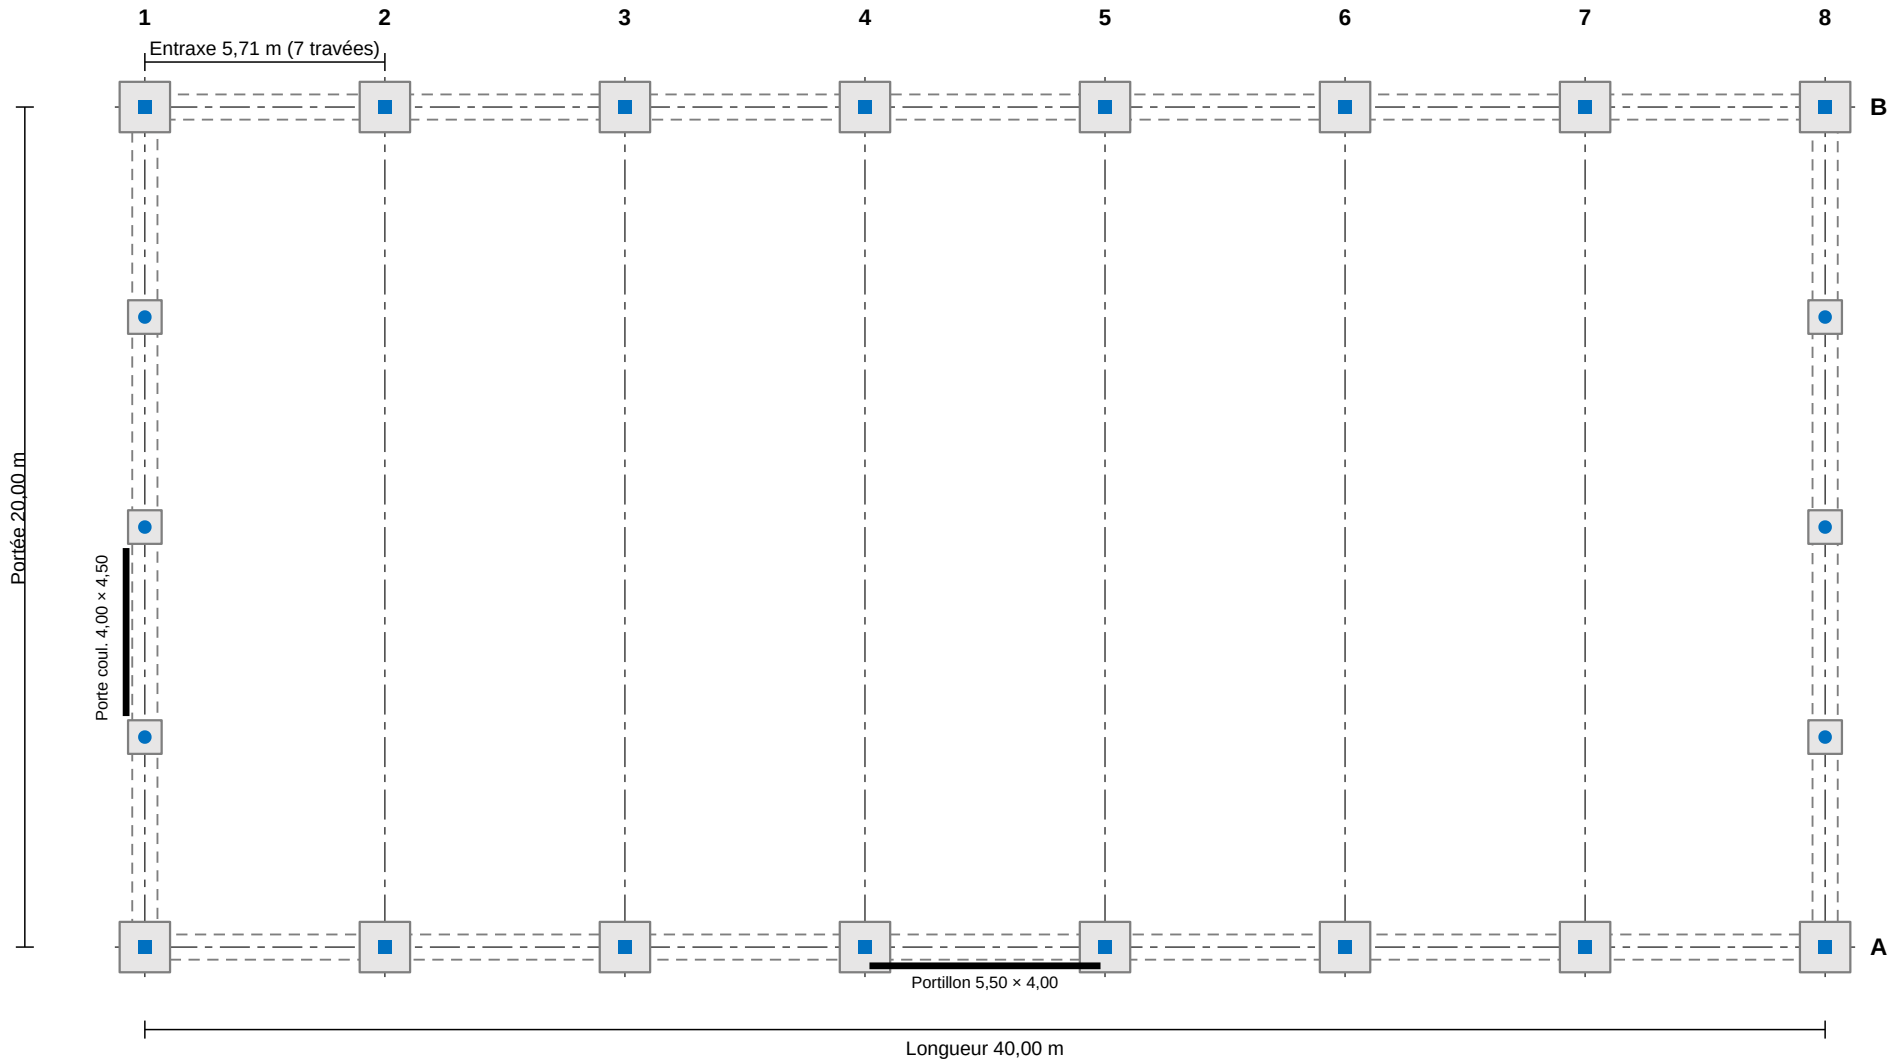


VUE EN PLAN – IMPLANTATION	**Planche n° 1 / 10**	Date : 04/11/2026
Bâtiment industriel – Abidjan · Gabarit 20 × 40 : portée 20,00 m × longueur 40,00 m – H sablière 6,00 m – pente 16,0 % – Portique IPE avec jarrets – façade : Bardage bac acier	**ESQUISSE NON CONTRACTUELLE**	
Couleurs : charpente en bleu · contreventements en orange · béton en gris · aciers en rouge · maçonnerie en marron clair · cotes et baies en noir · translucides hachurés en bleu clair · remblai en latérite	**BON POUR ACCORD**	
Poteaux de portique ■ IPE 330 sur semelles 120 × 120 ; poteaux de pignon ● IPE 220 sur semelles 80 × 80 ; semelles filantes en pointillés.	Date :	
	Signature :	
Échelle automatique (même échelle en X et en Y) – cotes en mètres – EC3 / EC1 / BAEL 91 mod. 99 / EC2 – esquisse de prédimensionnement à confirmer par note de calcul.		

PLANCHE 2 / 10 – COUPE TRANSVERSALE – PORTIQUE TYPE

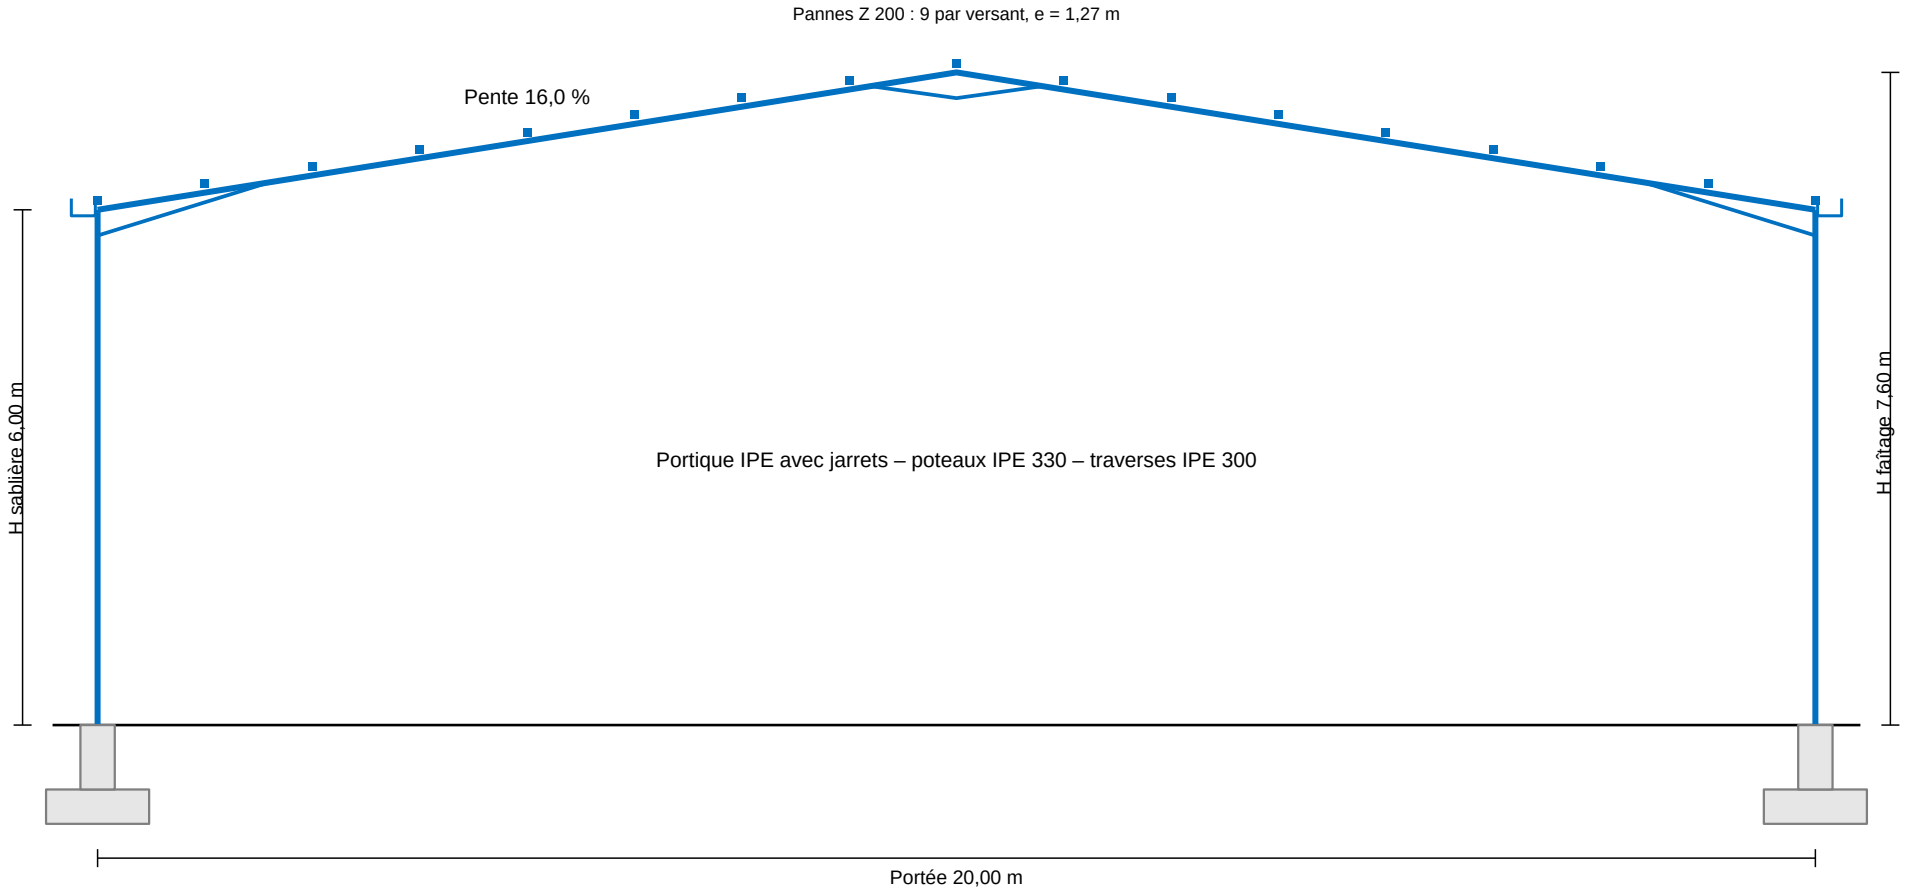


COUPE TRANSVERSALE – PORTIQUE TYPE	Planche n° 2 / 10	Date : 04/11/2026
Bâtiment industriel – Abidjan · Gabarit 20 × 40 : portée 20,00 m × longueur 40,00 m – H sablière 6,00 m – pente 16,0 % – Portique IPE avec jarrets – façade : Bardage bac acier	ESQUISSE NON CONTRACTUELLE	
Couleurs : charpente en bleu · contreventements en orange · béton en gris · aciers en rouge · maçonnerie en marron clair · cotes et baies en noir · translucides hachurés en bleu clair · remblai en latérite	BON POUR ACCORD	
Croix de Saint-André dans les travées d'extrémité et une travée sur 5 (3 travées). Lisses C 200 e = 1,80 m.	Date :	
	Signature :	
Échelle automatique (même échelle en X et en Y) – cotes en mètres – EC3 / EC1 / BAEL 91 mod. 99 / EC2 – esquisse de prédimensionnement à confirmer par note de calcul.		

PLANCHE 3 / 10 – ÉLÉVATION LONG-PAN

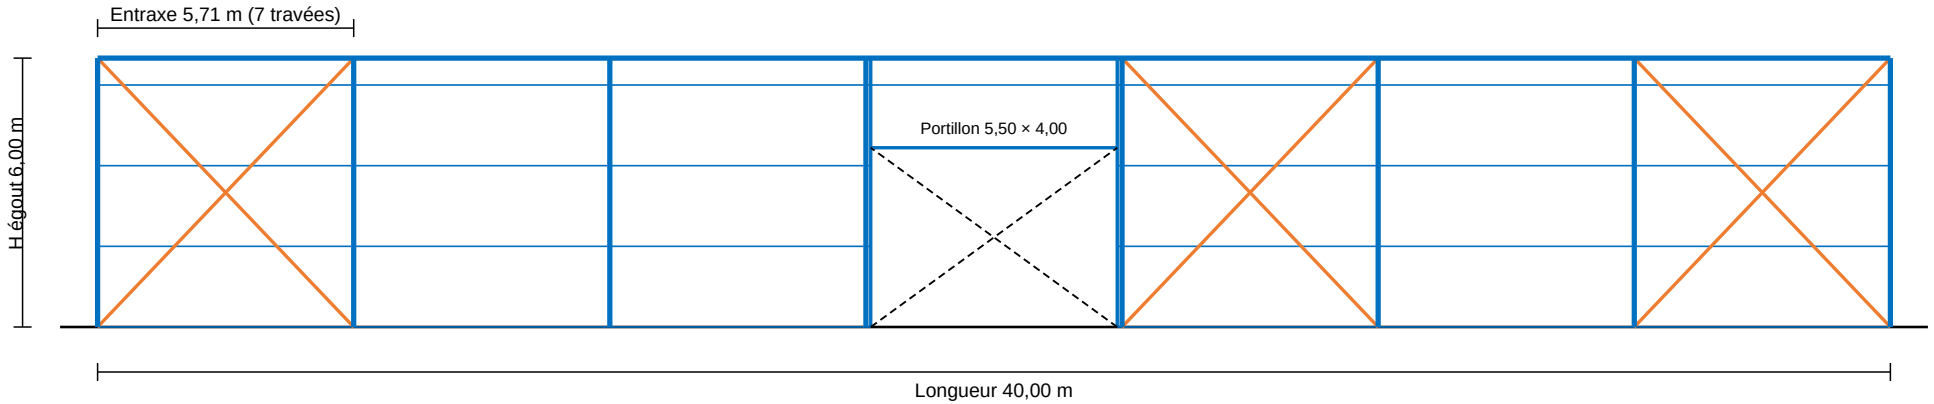


ÉLÉVATION LONG-PAN	**Planche n° 3 / 10**	Date : 04/11/2026
Bâtiment industriel – Abidjan · Gabarit 20 × 40 : portée 20,00 m × longueur 40,00 m – H sablière 6,00 m – pente 16,0 % – Portique IPE avec jarrets – façade : Bardage bac acier	**ESQUISSE NON CONTRACTUELLE**	
Couleurs : charpente en bleu · contreventements en orange · béton en gris · aciers en rouge · maçonnerie en marron clair · cotes et baies en noir · translucides hachurés en bleu clair · remblai en latérite	**BON POUR ACCORD**	
Croix de Saint-André dans les travées d'extrémité et une travée sur 5 (3 travées). Lisses C 200 e = 1,80 m.	Date :	
	Signature :	
Échelle automatique (même échelle en X et en Y) – cotes en mètres – EC3 / EC1 / BAEL 91 mod. 99 / EC2 – esquisse de prédimensionnement à confirmer par note de calcul.		

PLANCHE 4 / 10 – ÉLÉVATION PIGNON

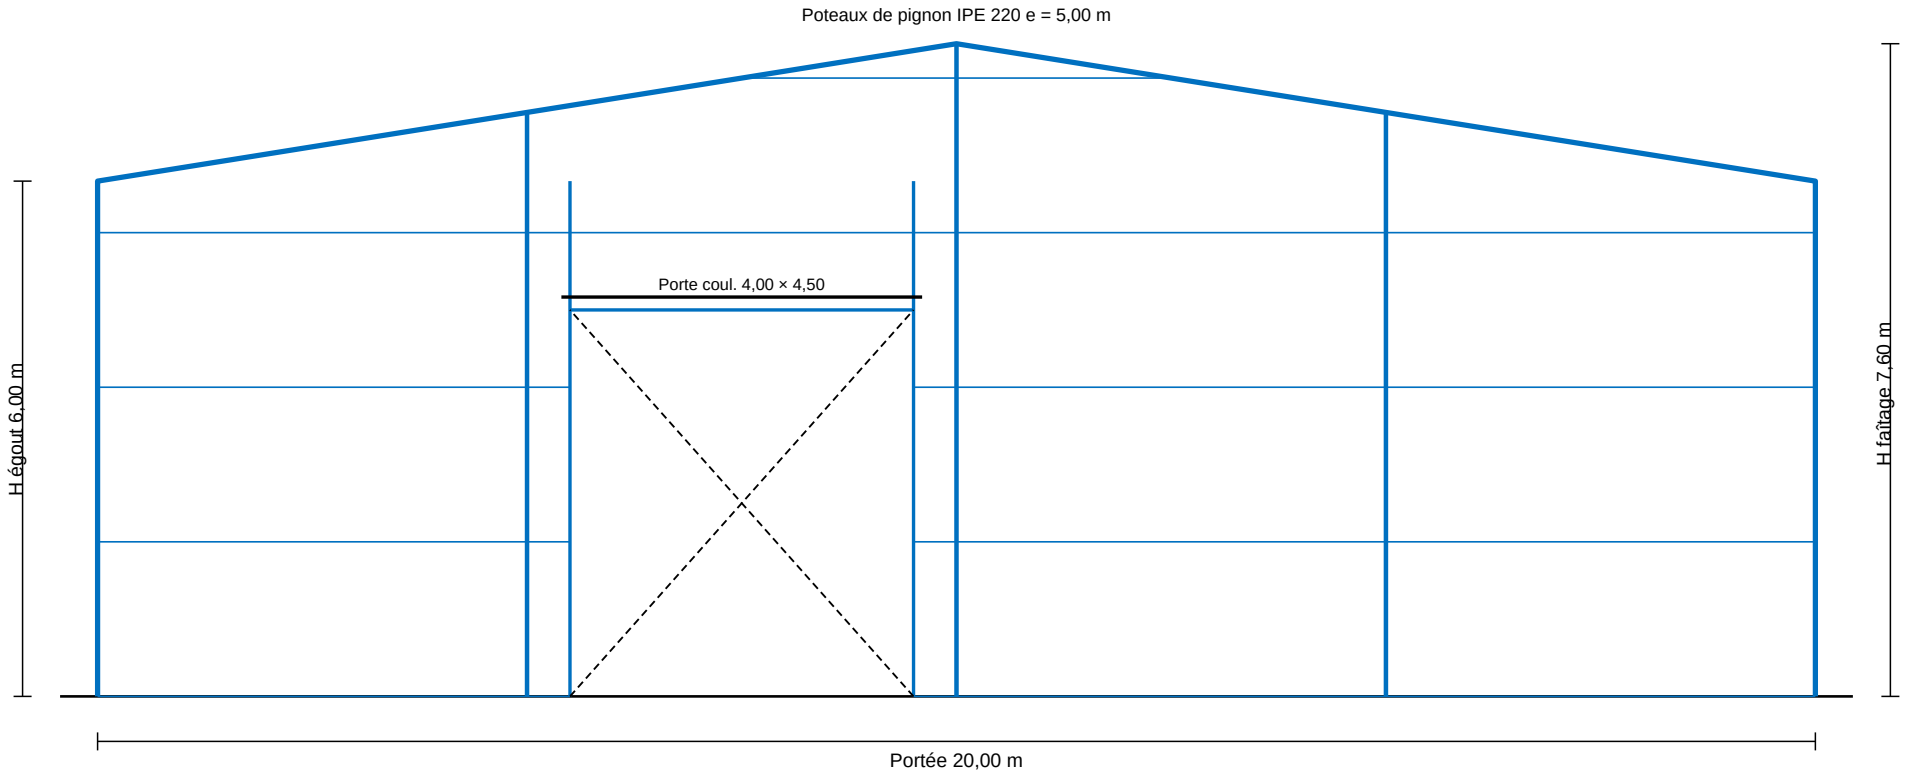


ÉLÉVATION PIGNON	**Planche n° 4 / 10**	Date : 04/11/2026
Bâtiment industriel – Abidjan · Gabarit 20 × 40 : portée 20,00 m × longueur 40,00 m – H sablière 6,00 m – pente 16,0 % – Portique IPE avec jarrets – façade : Bardage bac acier	**ESQUISSE NON CONTRACTUELLE**	
Couleurs : charpente en bleu · contreventements en orange · béton en gris · aciers en rouge · maçonnerie en marron clair · cotes et baies en noir · translucides hachurés en bleu clair · remblai en latérite	**BON POUR ACCORD**	
Croix de Saint-André dans les travées d'extrémité et une travée sur 5 (3 travées). Lisses C 200 e = 1,80 m.	Date :	
	Signature :	
Échelle automatique (même échelle en X et en Y) – cotes en mètres – EC3 / EC1 / BAEL 91 mod. 99 / EC2 – esquisse de prédimensionnement à confirmer par note de calcul.		

PLANCHE 5 / 10 – VUE EN PLAN TOITURE – CALEPINAGE

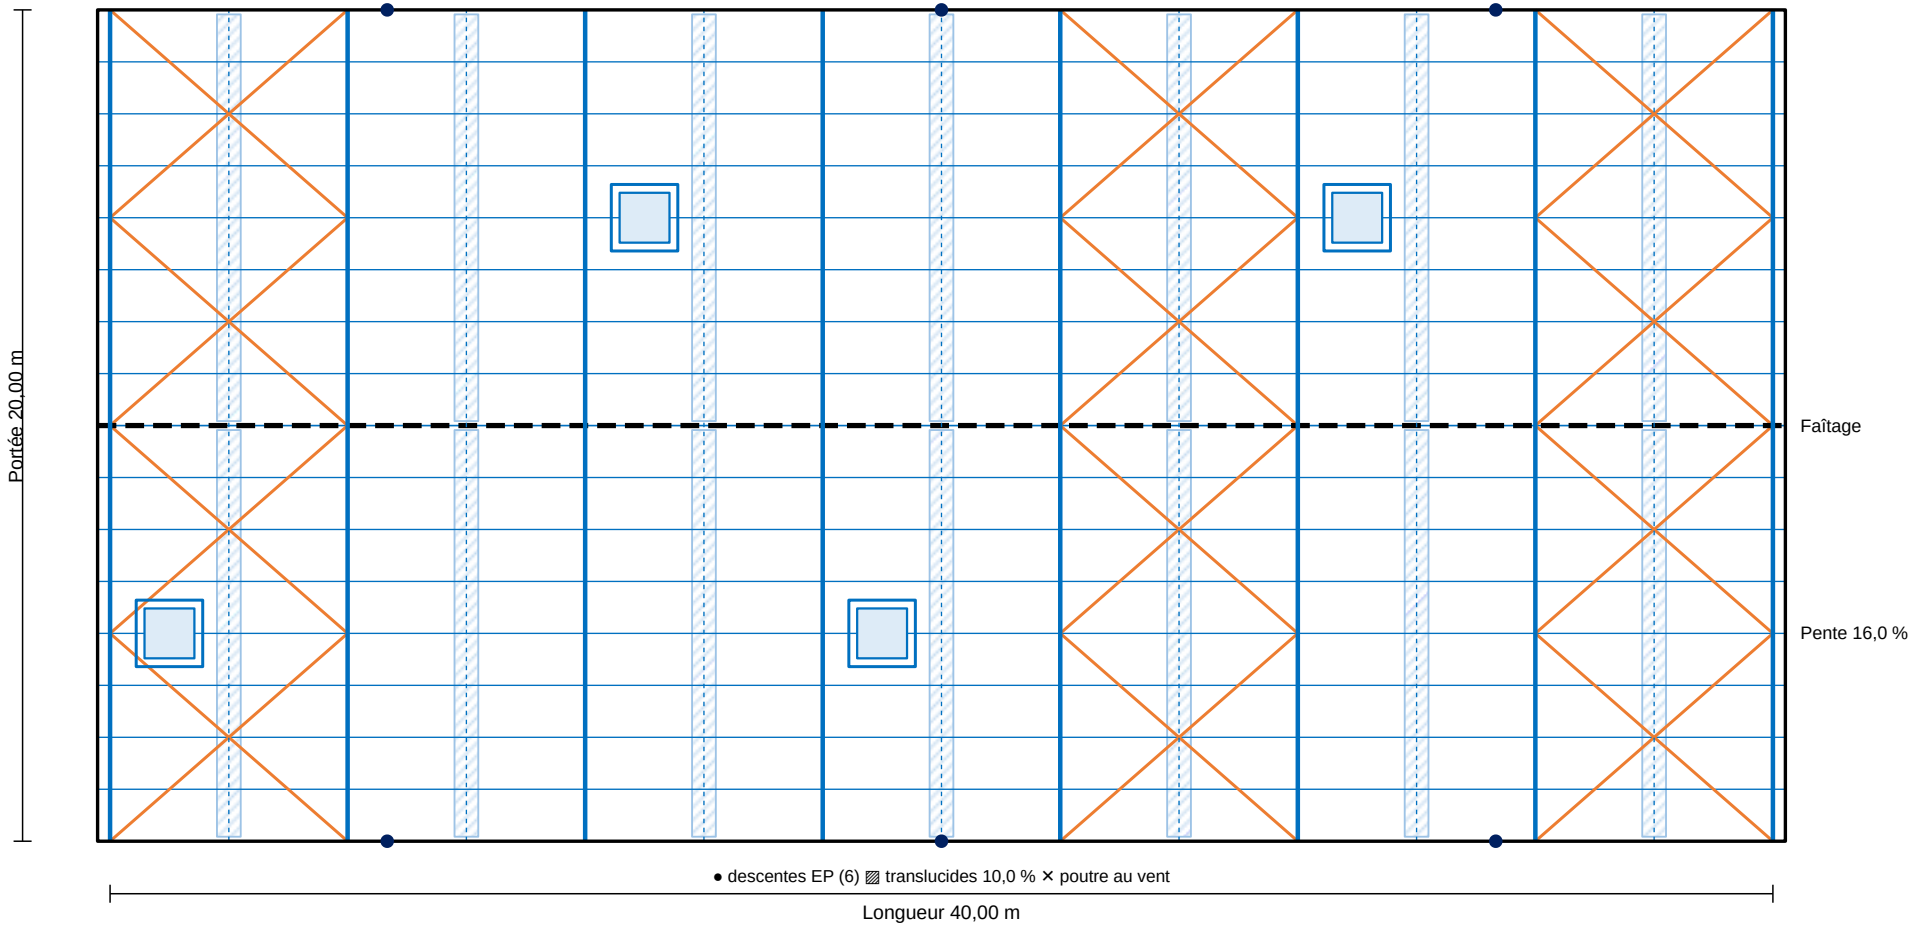

VUE EN PLAN TOITURE – CALEPINAGE	Planche n° 5 / 10	Date : 04/11/2026
Bâtiment industriel – Abidjan · Gabarit 20 × 40 : portée 20,00 m × longueur 40,00 m – H sablière 6,00 m – pente 16,0 % – Portique IPE avec jarrets – façade : Bardage bac acier	ESQUISSE NON CONTRACTUELLE	
Couleurs : charpente en bleu · contreventements en orange · béton en gris · aciers en rouge · maçonnerie en marron clair · cotes et baies en noir · translucides hachurés en bleu clair · remblai en latérite	BON POUR ACCORD	
Translucides : 10 % – skydomes : 4 – descentes EP : 6 – poutre au vent : 3 travées – liernes : 1 ligne(s) par travée.	Date :	
	Signature :	
Échelle automatique (même échelle en X et en Y) – cotes en mètres – EC3 / EC1 / BAEL 91 mod. 99 / EC2 – esquisse de prédimensionnement à confirmer par note de calcul.		

PLANCHE 6 / 10 – COUPE DE FONDATION ET DALLAGE (DÉTAIL)

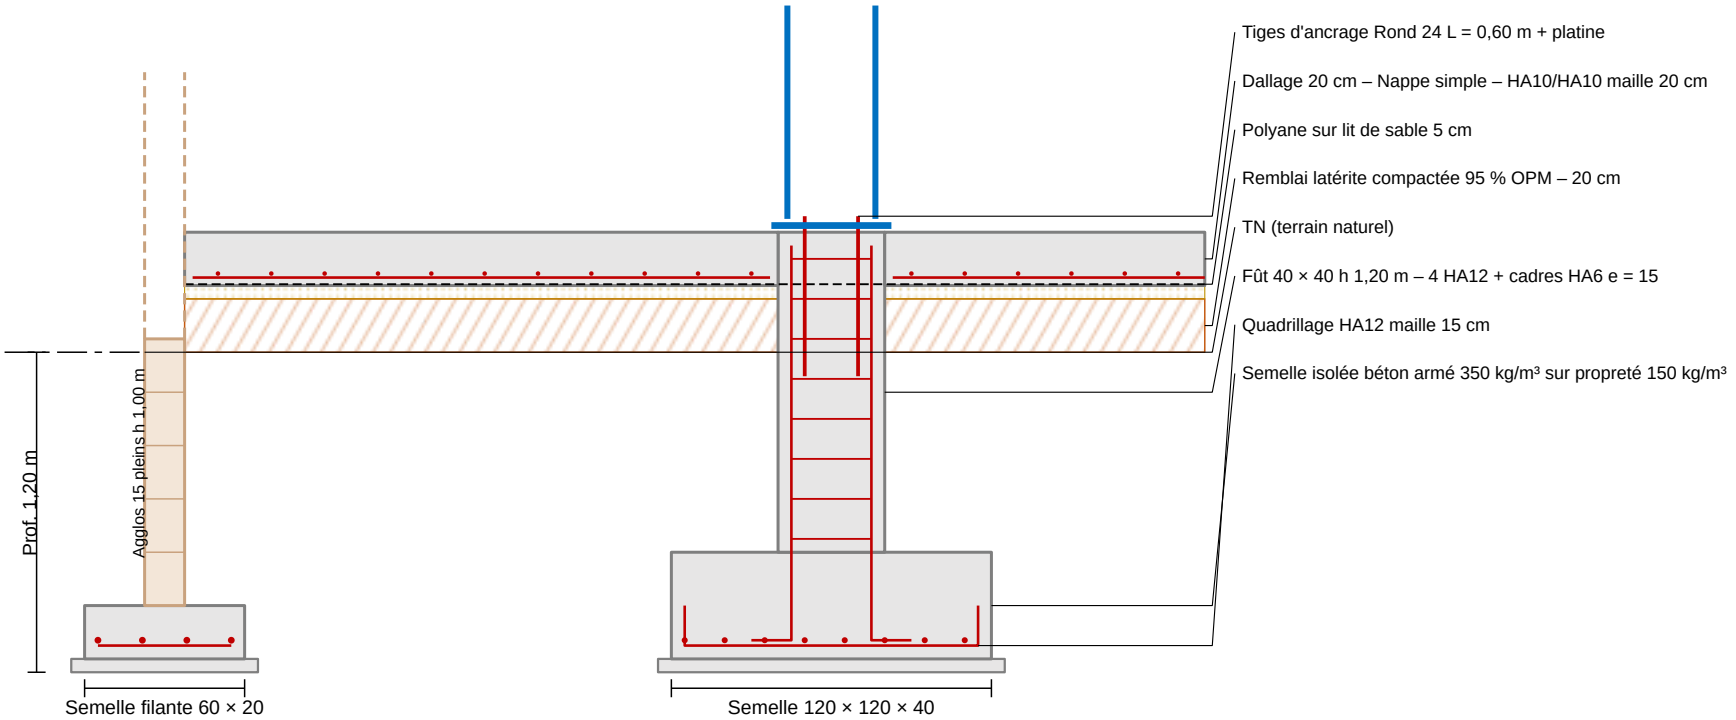

Filants 4 HA10 + rép. HA8 e = 20 cm

COUPE DE FONDATION ET DALLAGE (DÉTAIL)	**Planche n° 6 / 10**	Date : 04/11/2026
Bâtiment industriel – Abidjan · Gabarit 20 × 40 : portée 20,00 m × longueur 40,00 m – H sablière 6,00 m – pente 16,0 % – Portique IPE avec jarrets – façade : Bardage bac acier	**ESQUISSE NON CONTRACTUELLE**	
Couleurs : charpente en bleu · contreventements en orange · béton en gris · aciers en rouge · maçonnerie en marron clair · cotes et baies en noir · translucides hachurés en bleu clair · remblai en latérite	**BON POUR ACCORD**	
Aciers : semelles isolées HA12 maille 15 cm ; fûts 4 HA12 + cadres HA6 e = 15 cm ; semelle filante 4 HA10 + HA8 e = 20 cm ; dallage Nappe simple HA10 (X) / HA10 (Y), maille 20 cm.	Date :	
	Signature :	
Échelle automatique (même échelle en X et en Y) – cotes en mètres – EC3 / EC1 / BAEL 91 mod. 99 / EC2 – esquisse de prédimensionnement à confirmer par note de calcul.		


SANS OBJET : façade en bardage bac acier

(vue affichée en « Agglos 15 creux » ou « Mixte »)


ÉLÉVATION MUR AGGLOS – PANNEAU TYPE	**Planche n° 7 / 10**	Date : 04/11/2026
Bâtiment industriel – Abidjan · Gabarit 20 × 40 : portée 20,00 m × longueur 40,00 m – H sablière 6,00 m – pente 16,0 % – Portique IPE avec jarrets – façade : Bardage bac acier	**ESQUISSE NON CONTRACTUELLE**	
Couleurs : charpente en bleu · contreventements en orange · béton en gris · aciers en rouge · maçonnerie en marron clair · cotes et baies en noir · translucides hachurés en bleu clair · remblai en latérite	**BON POUR ACCORD**	
Sections : chaînages 15 × 20 cm et raidisseurs 15 × 15 cm – 4 HA10 + cadres HA6 e = 20 cm ; linteaux idem avec appuis de 20 cm.	Date :	
	Signature :	
Échelle automatique (même échelle en X et en Y) – cotes en mètres – EC3 / EC1 / BAEL 91 mod. 99 / EC2 – esquisse de prédimensionnement à confirmer par note de calcul.		

PLANCHE 8 / 10 – VUE D'ENSEMBLE – PERSPECTIVES ET PLAN DE CHARPENTE


BÂTIMENT TERMINÉ

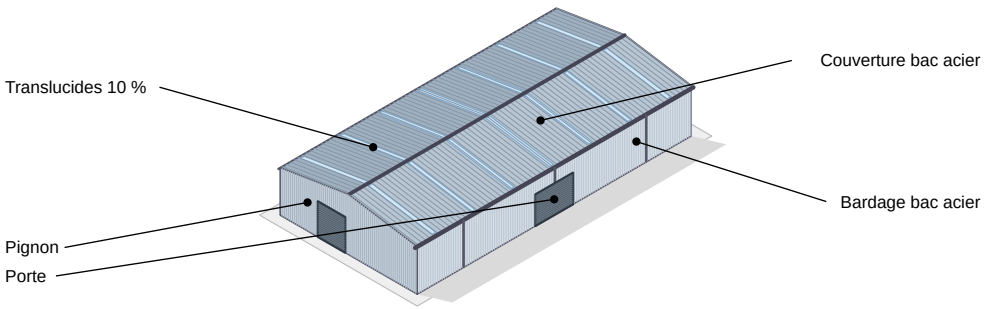


OSSATURE MÉTALLIQUE

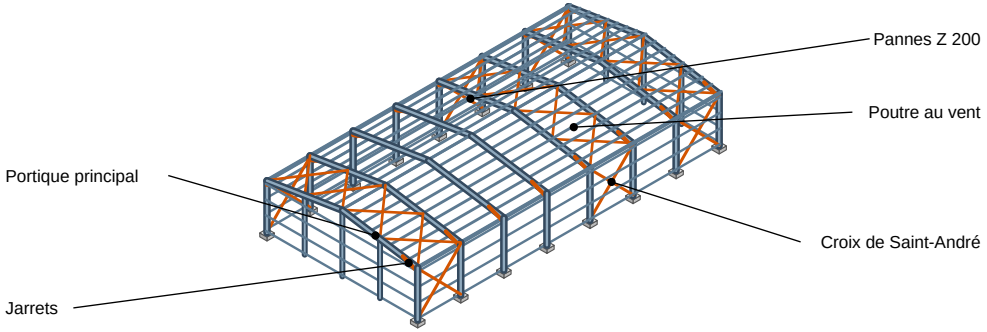

ÉLÉVATIONS LONG-PAN ET PIGNON

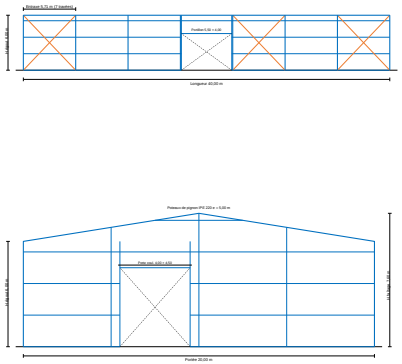

PLAN DE CHARPENTE DE TOITURE

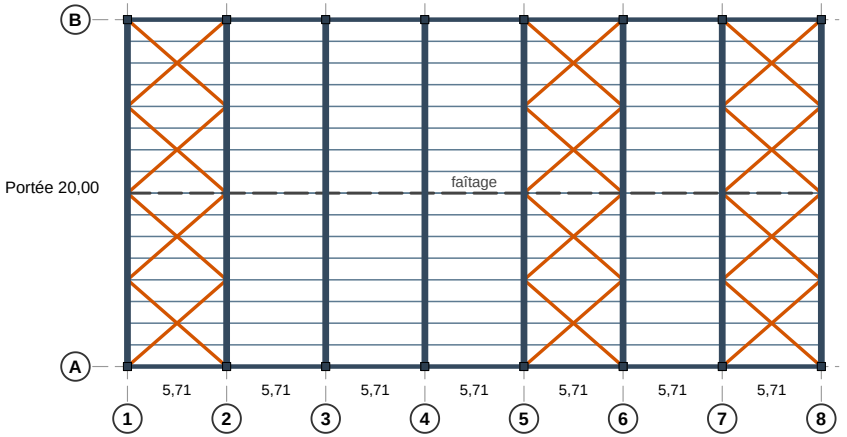


Longueur 40,00 m – 7 travées de 5,71 m

VUE D'ENSEMBLE – PERSPECTIVES ET PLAN DE CHARPENTE	Planche n° 8 / 10	Date : 04/11/2026
Bâtiment industriel – Abidjan · Gabarit 20 × 40 : portée 20,00 m × longueur 40,00 m – H sablière 6,00 m – pente 16,0 % – Portique IPE avec jarrets – façade : Bardage bac acier	ESQUISSE NON CONTRACTUELLE	
Couleurs : charpente en bleu · contreventements en orange · béton en gris · aciers en rouge · maçonnerie en marron clair · cotes et baies en noir · translucides hachurés en bleu clair · remblai en latérite	BON POUR ACCORD	
Perspectives isométriques sans échelle. Ossature : poteaux IPE 330, traverses IPE 300, pannes Z 200, lisses C 200, contreventements en orange.	Date :	
	Signature :	
Perspectives et détails sans échelle – cotes en mètres – EC3 / EC1 / BAEL 91 mod. 99 / EC2 – esquisse de prédimensionnement à confirmer par note de calcul.		

PLANCHE 9 / 10 – ASSEMBLAGE ÉCLATÉ ET NOMENCLATURE

ASSEMBLAGE ÉCLATÉ DE L'OSSATURE

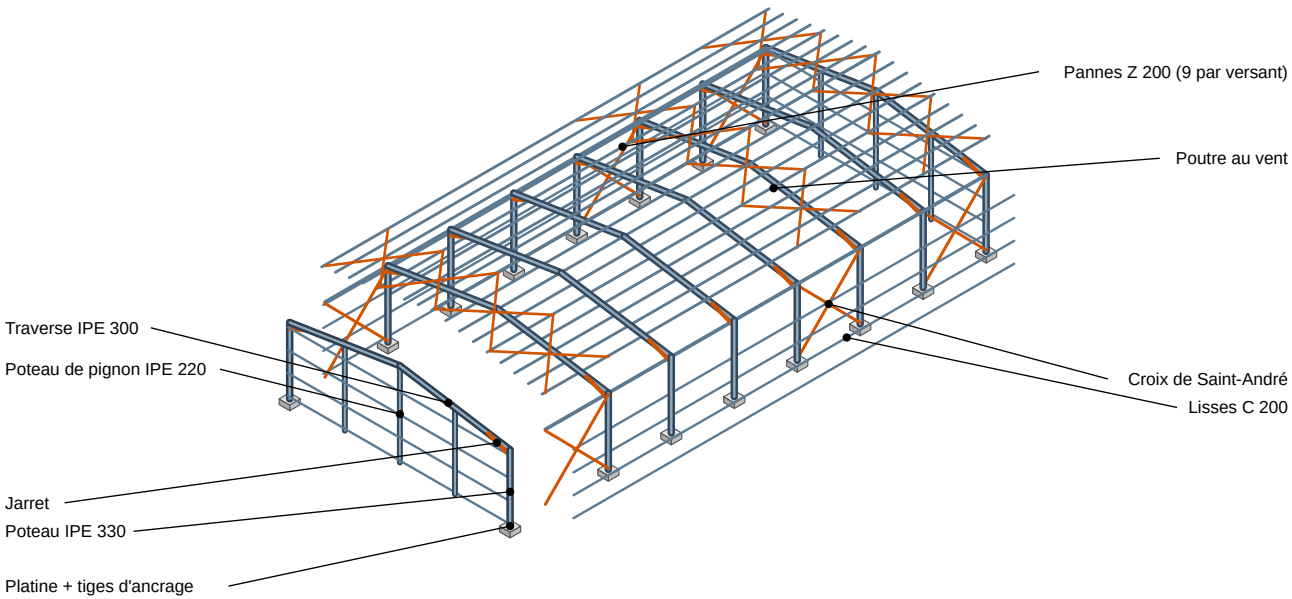

NOMENCLATURE DES MATÉRIAUX


Rep.	Désignation	Profil	Nb	L (m)	Poids (kg)
A	Poteaux de rive	IPE 330	16	6,00	4 714
B	Traverses (2 versants)	IPE 300	8	20,25	6 838
B'	Jarrets	IPE 300	16	2,00	1 350
C	Poteaux de pignon	IPE 220	6	7,07	1 111
D	Pannes	Z 200	18	40,60	3 800
E	Lisses de bardage	C 200	82	5,71	2 577
F	Croix de Saint-André	L 60x6	12	8,29	539
G	Poutre au vent	L 50x5	24	7,63	691
H	Liernes et bretelles	Rond 12	126	1,27	142
I	Platines de pied	PL 450×350×20	16	–	395
J	Tiges d'ancrage	Rond 24	64	0,60	136
K	Boulons HR M20	HR M20	192	–	86
TOTAL INDICATIF (hors chutes)					**22 379 kg**

Soit ≈ 28,0 kg/m². Métré détaillé : feuille QUANTITATIF_CHARPENTE du classeur.


ASSEMBLAGE ÉCLATÉ ET NOMENCLATURE	**Planche n° 9 / 10**	Date : 04/11/2026
Bâtiment industriel – Abidjan · Gabarit 20 × 40 : portée 20,00 m × longueur 40,00 m – H sablière 6,00 m – pente 16,0 % – Portique IPE avec jarrets – façade : Bardage bac acier	**ESQUISSE NON CONTRACTUELLE**	
Couleurs : charpente en bleu · contreventements en orange · béton en gris · aciers en rouge · maçonnerie en marron clair · cotes et baies en noir · translucides hachurés en bleu clair · remblai en latérite	**BON POUR ACCORD**	
Vue éclatée : pannes et poutre au vent soulevées, portique de rive et lisses du long-pan avant écartés pour la lisibilité. Nomenclature indicative.	Date :	
	Signature :	
Perspectives et détails sans échelle – cotes en mètres – EC3 / EC1 / BAEL 91 mod. 99 / EC2 – esquisse de prédimensionnement à confirmer par note de calcul.		

PLANCHE 10 / 10 – DÉTAILS D'ASSEMBLAGE


PIED DE POTEAU (PERSPECTIVE)

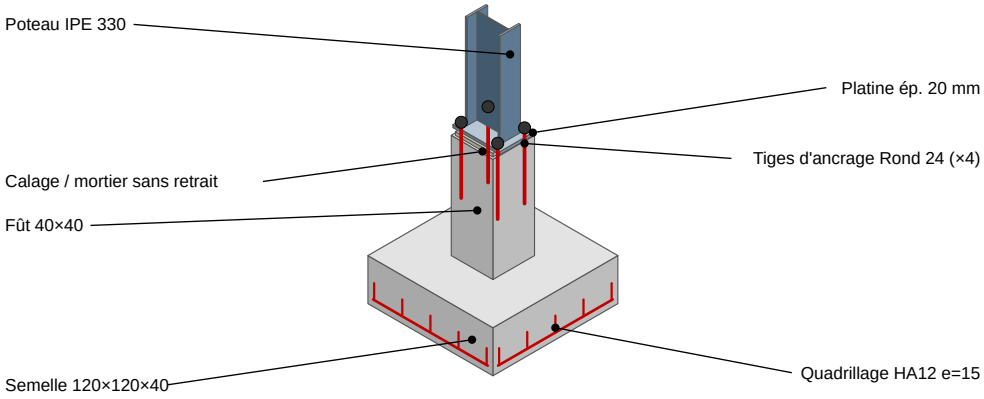


ASSEMBLAGE DE FAÎTAGE

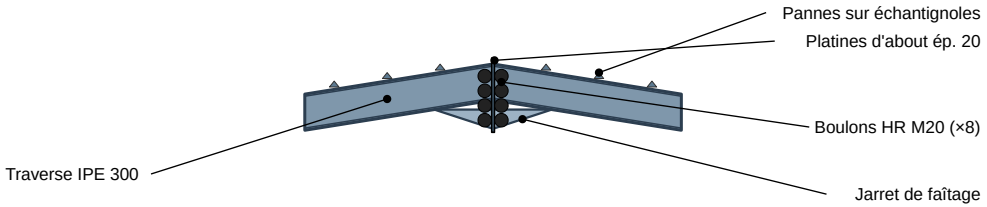

JARRET – ASSEMBLAGE POTEAU-TRAVERSE

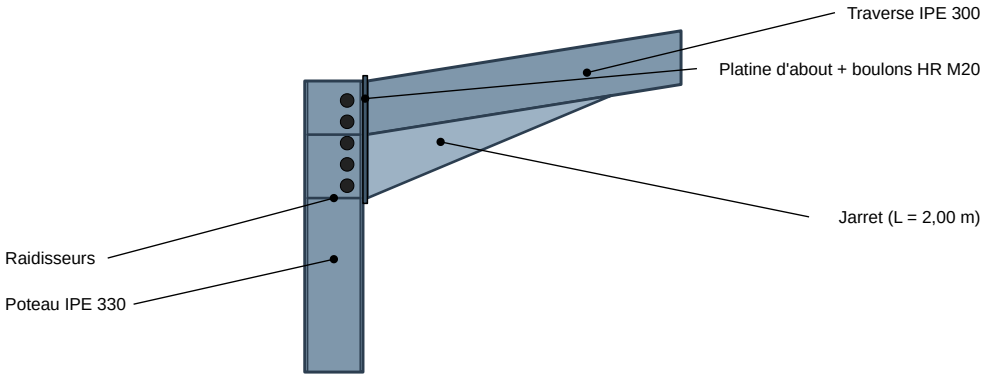

ATTACHE DE CONTREVENTEMENT

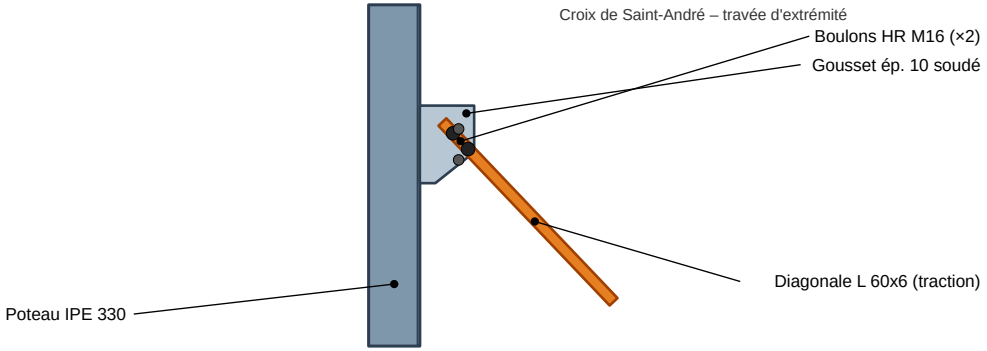

DÉTAILS D'ASSEMBLAGE	Planche n° 10 / 10	Date : 04/11/2026
Bâtiment industriel – Abidjan · Gabarit 20 × 40 : portée 20,00 m × longueur 40,00 m – H sablière 6,00 m – pente 16,0 % – Portique IPE avec jarrets – façade : Bardage bac acier	ESQUISSE NON CONTRACTUELLE	
Couleurs : charpente en bleu · contreventements en orange · béton en gris · aciers en rouge · maçonnerie en marron clair · cotes et baies en noir · translucides hachurés en bleu clair · remblai en latérite	BON POUR ACCORD	
Détails types sans échelle – épaisseurs et boulonnerie à confirmer par la note de calcul des assemblages (EC3-1-8).	Date :	
	Signature :	
Perspectives et détails sans échelle – cotes en mètres – EC3 / EC1 / BAEL 91 mod. 99 / EC2 – esquisse de prédimensionnement à confirmer par note de calcul.		