




PLANCHE 1 / 7 – VUE EN PLAN – IMPLANTATION

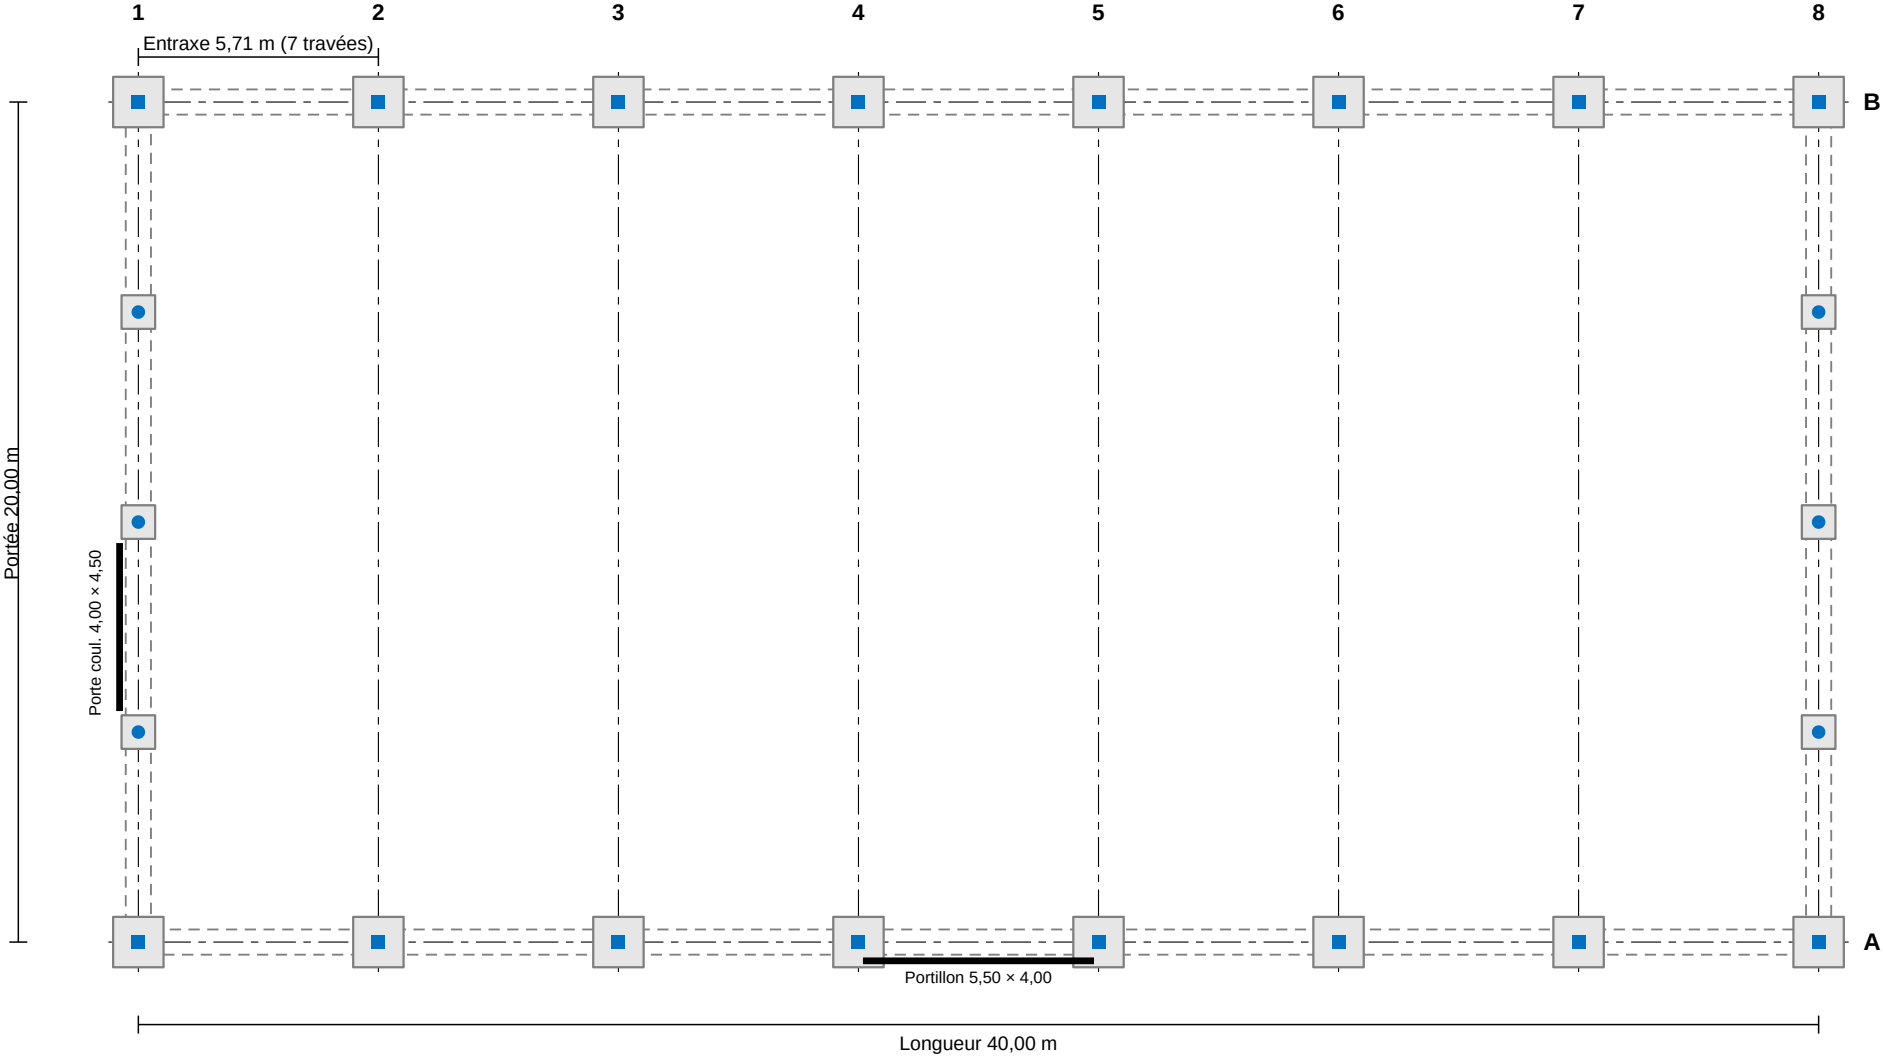


VUE EN PLAN – IMPLANTATION	Planche n° 1 / 7	Date : 06/10/2026
Bâtiment industriel – Abidjan · Gabarit 20 × 40 : portée 20,00 m × longueur 40,00 m – H sablière 6,00 m – pente 16,0 % – Portique IPE avec jarrets – façade : Bardage bac acier	ESQUISSE NON CONTRACTUELLE	
Couleurs : charpente en bleu · contreventements en orange · béton en gris · aciers en rouge · maçonnerie en marron clair · cotes et baies en noir · translucides hachurés en bleu clair · remblai en latérite	BON POUR ACCORD	
Poteaux de portique ■ IPE 330 sur semelles 120 × 120 ; poteaux de pignon ● IPE 220 sur semelles 80 × 80 ; semelles filantes en pointillés.	Date :	
	Signature :	
Échelle automatique (même échelle en X et en Y) – cotes en mètres – EC3 / EC1 / BAEL 91 mod. 99 / EC2 – esquisse de prédimensionnement à confirmer par note de calcul.		

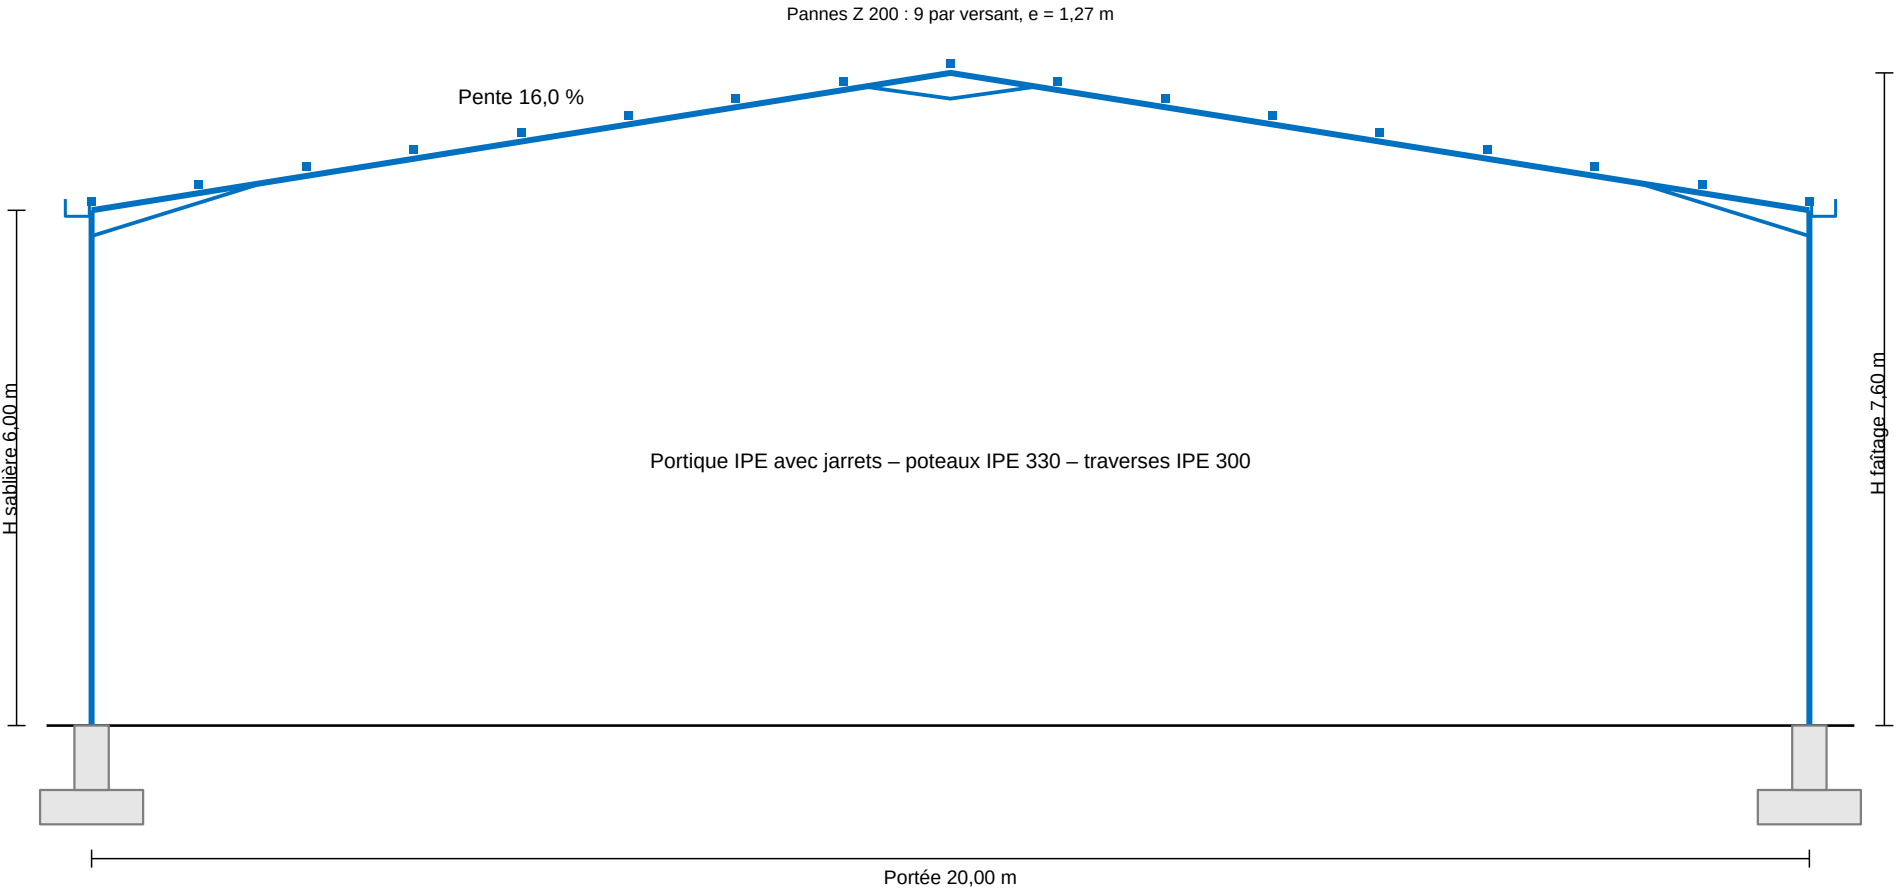


COUPE TRANSVERSALE – PORTIQUE TYPE	Planche n° 2 / 7	Date : 06/10/2026
Bâtiment industriel – Abidjan · Gabarit 20 × 40 : portée 20,00 m × longueur 40,00 m – H sablière 6,00 m – pente 16,0 % – Portique IPE avec jarrets – façade : Bardage bac acier	ESQUISSE NON CONTRACTUELLE	
Couleurs : charpente en bleu · contreventements en orange · béton en gris · aciers en rouge · maçonnerie en marron clair · cotes et baies en noir · translucides hachurés en bleu clair · remblai en latérite	BON POUR ACCORD	
Croix de Saint-André dans les travées d'extrémité et une travée sur 5 (3 travées). Lisses C 160 e = 1,80 m.	Date :	
	Signature :	
Échelle automatique (même échelle en X et en Y) – cotes en mètres – EC3 / EC1 / BAEL 91 mod. 99 / EC2 – esquisse de prédimensionnement à confirmer par note de calcul.		

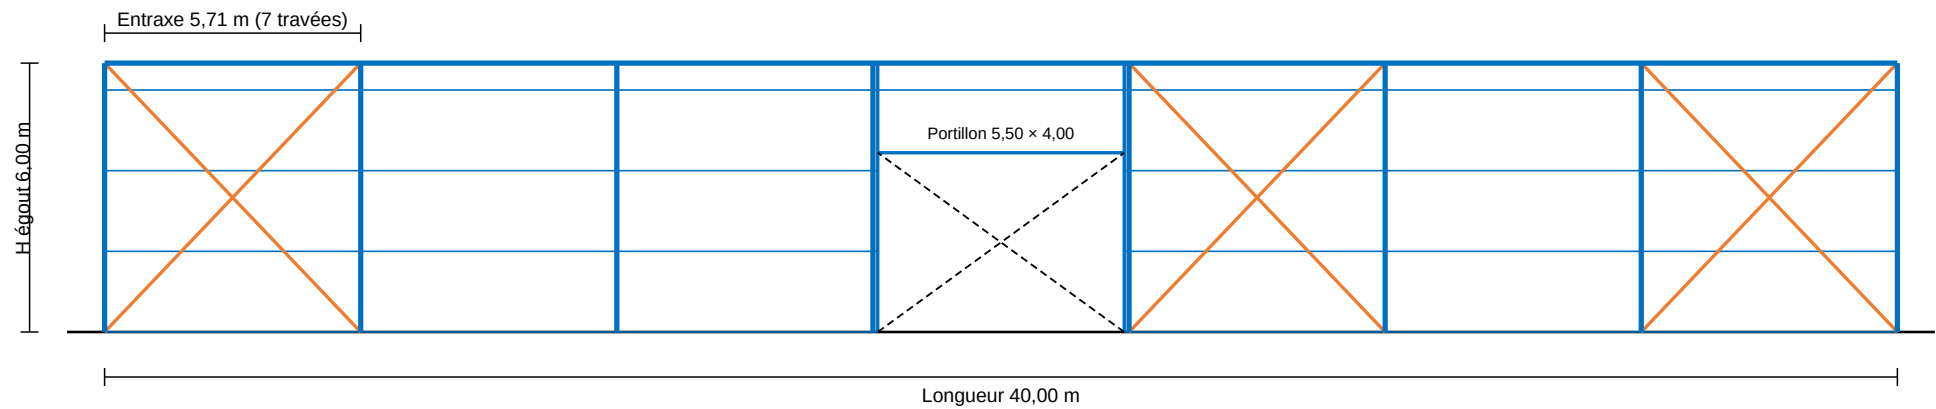

ÉLÉVATION LONG-PAN	Planche n° 3 / 7	Date : 06/10/2026
Bâtiment industriel – Abidjan · Gabarit 20 × 40 : portée 20,00 m × longueur 40,00 m – H sablière 6,00 m – pente 16,0 % – Portique IPE avec jarrets – façade : Bardage bac acier	ESQUISSE NON CONTRACTUELLE	
Couleurs : charpente en bleu · contreventements en orange · béton en gris · aciers en rouge · maçonnerie en marron clair · cotes et baies en noir · translucides hachurés en bleu clair · remblai en latérite	BON POUR ACCORD	
Croix de Saint-André dans les travées d'extrémité et une travée sur 5 (3 travées). Lisses C 160 e = 1,80 m.	Date :	
	Signature :	
Échelle automatique (même échelle en X et en Y) – cotes en mètres – EC3 / EC1 / BAEL 91 mod. 99 / EC2 – esquisse de prédimensionnement à confirmer par note de calcul.		

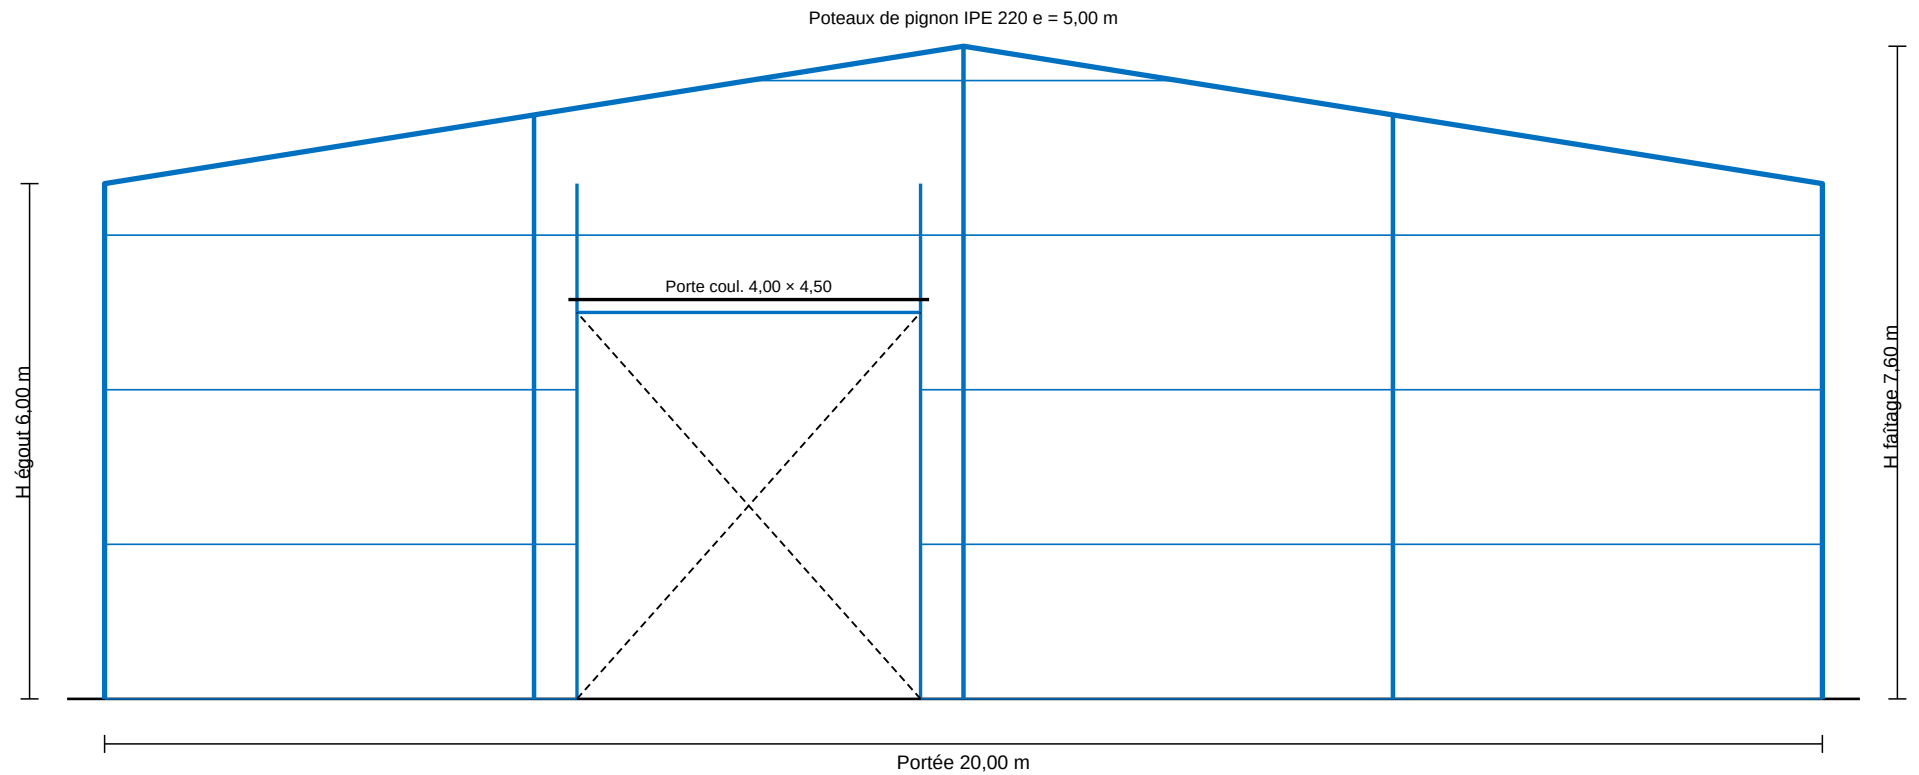


ÉLÉVATION PIGNON	Planche n° 4 / 7	Date : 06/10/2026
Bâtiment industriel – Abidjan · Gabarit 20 × 40 : portée 20,00 m × longueur 40,00 m – H sablière 6,00 m – pente 16,0 % – Portique IPE avec jarrets – façade : Bardage bac acier	ESQUISSE NON CONTRACTUELLE	
Couleurs : charpente en bleu · contreventements en orange · béton en gris · aciers en rouge · maçonnerie en marron clair · cotes et baies en noir · translucides hachurés en bleu clair · remblai en latérite	BON POUR ACCORD	
Croix de Saint-André dans les travées d'extrémité et une travée sur 5 (3 travées). Lisses C 160 e = 1,80 m.	Date :	
	Signature :	
Échelle automatique (même échelle en X et en Y) – cotes en mètres – EC3 / EC1 / BAEL 91 mod. 99 / EC2 – esquisse de prédimensionnement à confirmer par note de calcul.		

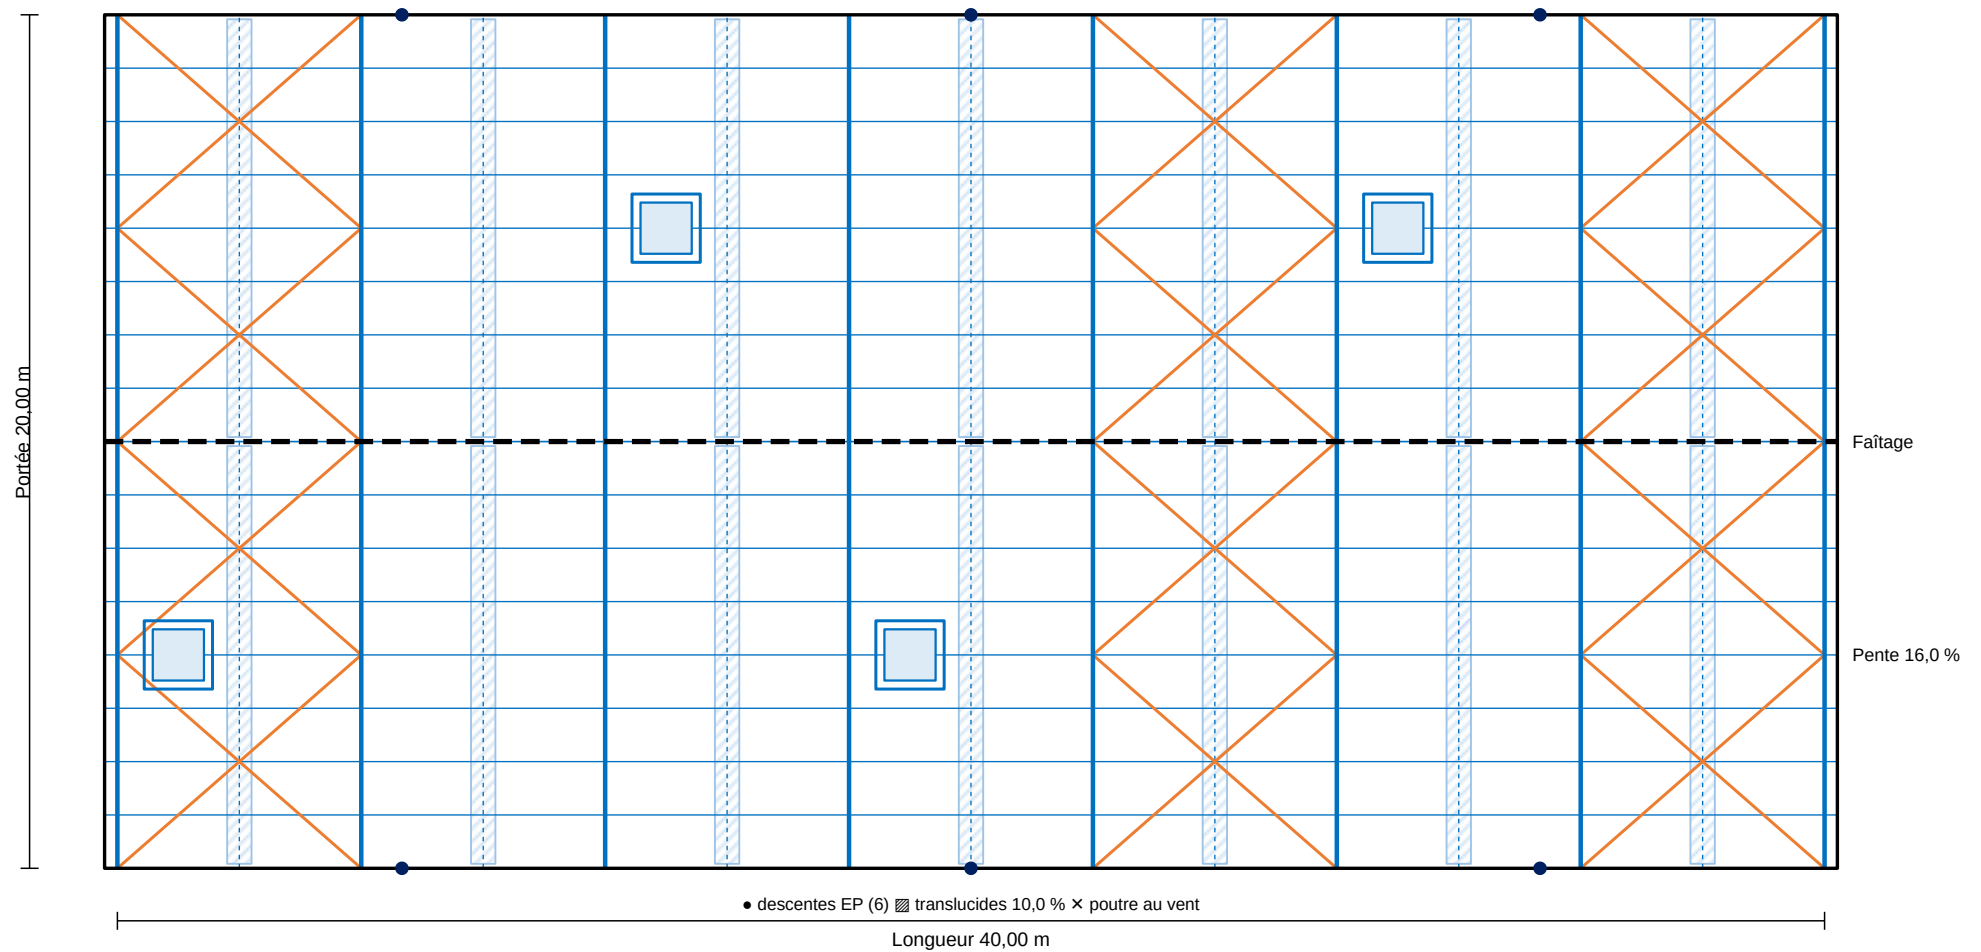

VUE EN PLAN TOITURE – CALEPINAGE	Planche n° 5 / 7	Date : 06/10/2026
Bâtiment industriel – Abidjan · Gabarit 20 × 40 : portée 20,00 m × longueur 40,00 m – H sablière 6,00 m – pente 16,0 % – Portique IPE avec jarrets – façade : Bardage bac acier	ESQUISSE NON CONTRACTUELLE	
<i>Couleurs : charpente en bleu · contreventements en orange · béton en gris · aciers en rouge · maçonnerie en marron clair · cotes et baies en noir · translucides hachurés en bleu clair · remblai en latérite</i>	BON POUR ACCORD	
Translucides : 10 % – skydomes : 4 – descentes EP : 6 – poutre au vent : 3 travées – liernes : 1 ligne(s) par travée.	Date :	
	Signature :	
<i>Échelle automatique (même échelle en X et en Y) – cotes en mètres – EC3 / EC1 / BAEL 91 mod. 99 / EC2 – esquisse de prédimensionnement à confirmer par note de calcul.</i>		

PLANCHE 6 / 7 – COUPE DE FONDATION ET DALLAGE (DÉTAIL)

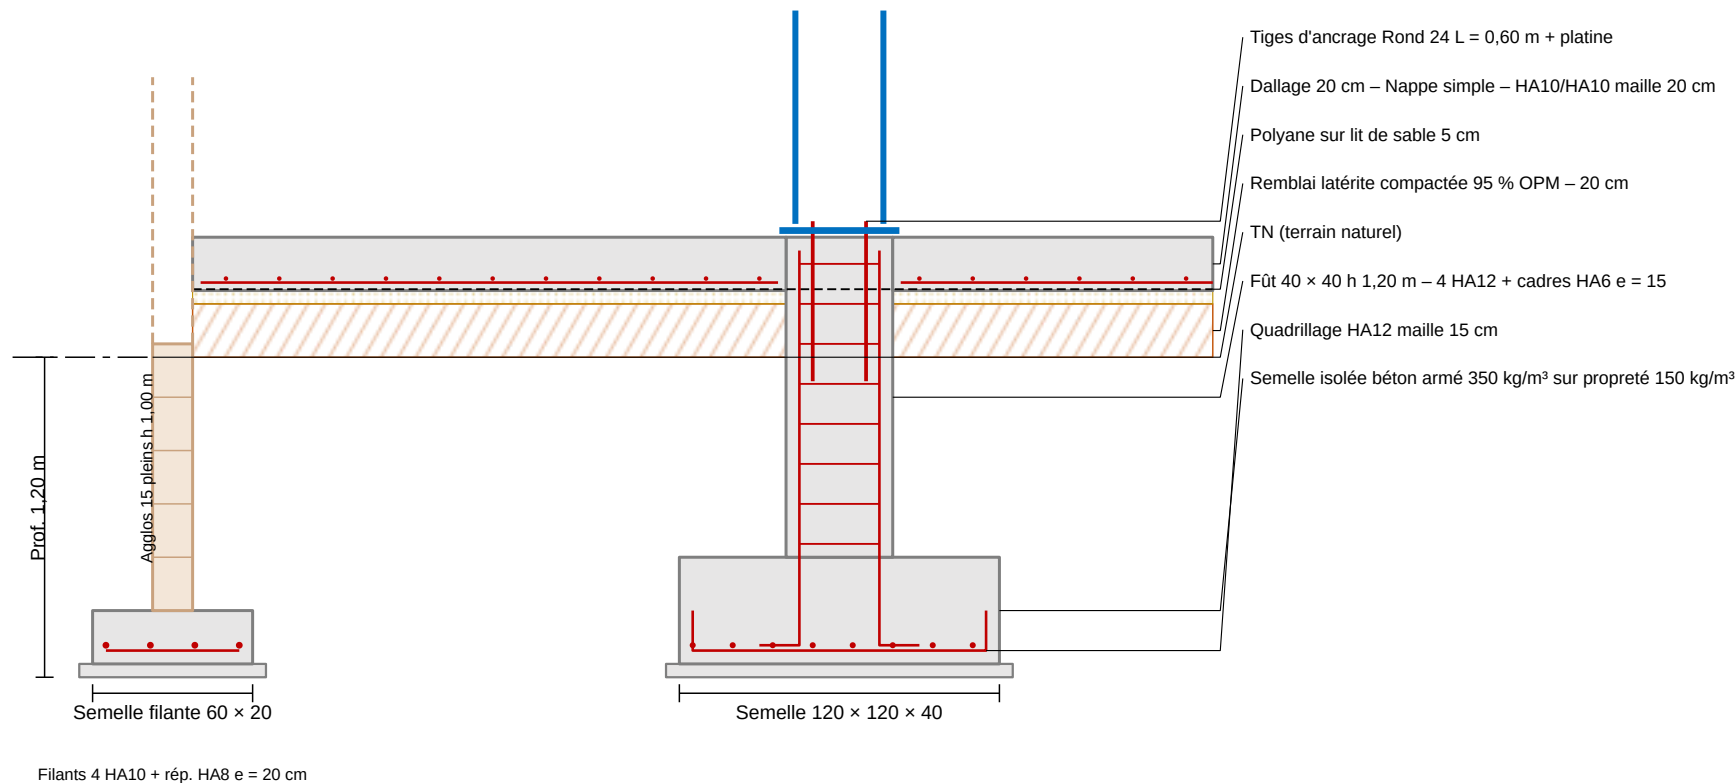

COUPE DE FONDATION ET DALLAGE (DÉTAIL)

Planche n° 6 / 7

Date :
06/10/2026

Bâtiment industriel – Abidjan · Gabarit 20 × 40 : portée 20,00 m × longueur 40,00 m – H sablière 6,00 m – pente 16,0 % – Portique IPE avec jarrets – façade : Bardage bac acier

ESQUISSE NON CONTRACTUELLE

Couleurs : charpente en bleu · contreventements en orange · béton en gris · aciers en rouge · maçonnerie en marron clair · cotes et baies en noir · translucides hachurés en bleu clair · remblai en latérite

BON POUR ACCORD

Aciers : semelles isolées HA12 maille 15 cm ; fûts 4 HA12 + cadres HA6 e = 15 cm ; semelle filante 4 HA10 + HA8 e = 20 cm ; dallage Nappe simple HA10 (X) / HA10 (Y), maille 20 cm.

Date :

Signature :

Échelle automatique (même échelle en X et en Y) – cotes en mètres – EC3 / EC1 / BAEL 91 mod. 99 / EC2 – esquisse de prédimensionnement à confirmer par note de calcul.

SANS OBJET : façade en bardage bac acier
(vue affichée en « Agglos 15 creux » ou « Mixte »)

ÉLÉVATION MUR AGGLOS – PANNEAU TYPE	Planche n° 7 / 7	Date : 06/10/2026
Bâtiment industriel – Abidjan · Gabarit 20 × 40 : portée 20,00 m × longueur 40,00 m – H sablière 6,00 m – pente 16,0 % – Portique IPE avec jarrets – façade : Bardage bac acier	ESQUISSE NON CONTRACTUELLE	
Couleurs : charpente en bleu · contreventements en orange · béton en gris · aciers en rouge · maçonnerie en marron clair · cotes et baies en noir · translucides hachurés en bleu clair · remblai en latérite	BON POUR ACCORD	
Sections : chaînages 15 × 20 cm et raidisseurs 15 × 15 cm – 4 HA10 + cadres HA6 e = 20 cm ; linteaux idem avec appuis de 20 cm.	Date :	
	Signature :	
Échelle automatique (même échelle en X et en Y) – cotes en mètres – EC3 / EC1 / BAEL 91 mod. 99 / EC2 – esquisse de prédimensionnement à confirmer par note de calcul.		